Agência Nacional do Petróleo

PERFIL COMPOSTO

1APS 0027A AP
PREFIXO

AMAPA SUNMARIN-27A
DESIGNACAO

LOCALIZACAO

QUADRANGULO: NB-22-V-IV -2-SE

AREA OU CAMPO:

BACIA: FOZ DO AMAZONAS

COORDENADAS DO ALVO
(OBJETIVO PRINCIPAL)

GEOGRAFICAS: LATITUDE: -4 19 29.82 N
LONGITUDE: 50 6 47.02 W

UTM: X= 10478108.7 M
Y= 598422.8 M MC= 51

33486 N E 10623 W

COORDENADAS DA BOCA
UTM: X=
Y= MC=

DATUM: PSAD-56

ELEVACOES
MR= 33.0 M CB= -95.0 M LINHA SISMICA:

PROFUNDIDADE
PERFURACAO: 2415.5 M PERFILAGEM: 2416.5 M PONTO DE TIRO:
(-2382.5 M)
FORMACAO: CACIPORE

DATAS

INICIO PERFURACAO	TERMINO PERFURACAO
22/12/78	03/03/79

RECLASSIFICACAO:
PRODUTOR SUBCOMERCIAL DE OLEO
(01)
DATA: 03/04/79

EQUIPAMENTO
SONDA N.: SS-5 OPERADOR: PETROBRAS

DATA DE ATUALIZACAO
28/08/02
AUTOR

OCORRENCIAS DE PETROLEO	TESTES DE FORMACAO	REVESTIMENTOS CANHONEIOS	TESTEMUNHOS	ZONAS PALENTOLOGICAS	CONTATOS
INDICIOS / ZONAS POTENC. PRODUTORAS	POROSIDADE E SATURACAO MEDIAS	PERDAS DE CIRCULACAO		CRONOESTRATIGRAFIA	

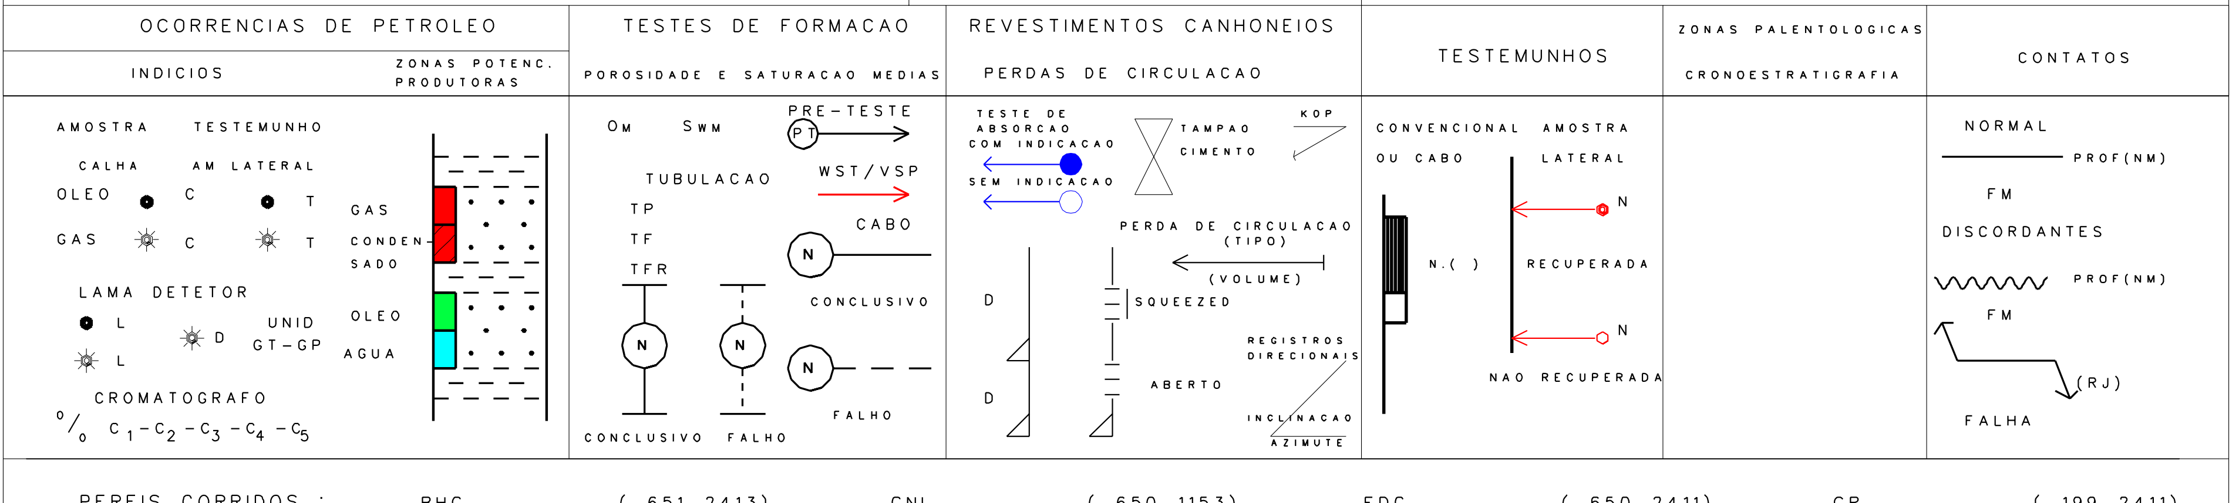

PERFIS CORRIDOS :							
BHC	(651-2413)	CNL	(650-1153)	FDC	(650-2411)	GR	(199-2411)
HDT	(1133-2373)	IES	(651-2416)				

KOP REVEST. TAMPOES CANHON. DIAM. POCO REG. DIREC. AMB.DEPOS.	INDICIOS DE H C		TESTES DE FORMACAO V S P	ESCALA 1/2000	TESTEMUNHOS PERDAS AM LATERAIS	ZONEAMENTO PALEONTOLOGICO CROESTRATIGRAFICO		DESCRICAO LITOLOGICA SUCINTA TOPO DE FORMACOES

Litologia / Lithology

- ▨ *conglomerado/conglomerate*
- ▨ *arenito/sandstone*
- ▨ *siltito/siltstone*
- ▨ *argilito/mudstone*
- ▨ *folhelho/shale*
- ▨ *calcirudito/calcirudite*
- ▨ *calcarenito/calcarenite*
- ▨ *coquina/coquina*
- ▨ *calcissiltito/calcisiltite*
- ▨ *calcilutito/calcilutite*
- ▨ *marga/marl*
- ▨ *calcáreo/limestone*
- ▨ *dolomita/dolomite*
- ▨ *sal/salt*
- ▨ *halita/halite*
- ▨ *carnalita/carnallite*
- ▨ *anidrita/anhydrite*
- ▨ *silvinita/sylvinite*
- ▨ *diabásio/diabase*
- ▨ *basalto/basalt*
- ▨ *tufo/tuff*
- ▨ *rochas metamórficas metamorphic rocks*
- ▨ *ígneas/igneous rocks*
- ▨ *brechas/breccia*
- ▨ *tilito/tillite*
- ▨ *diamictito/diamictite*

fonte: PETROBRAS
escala 1:2000